


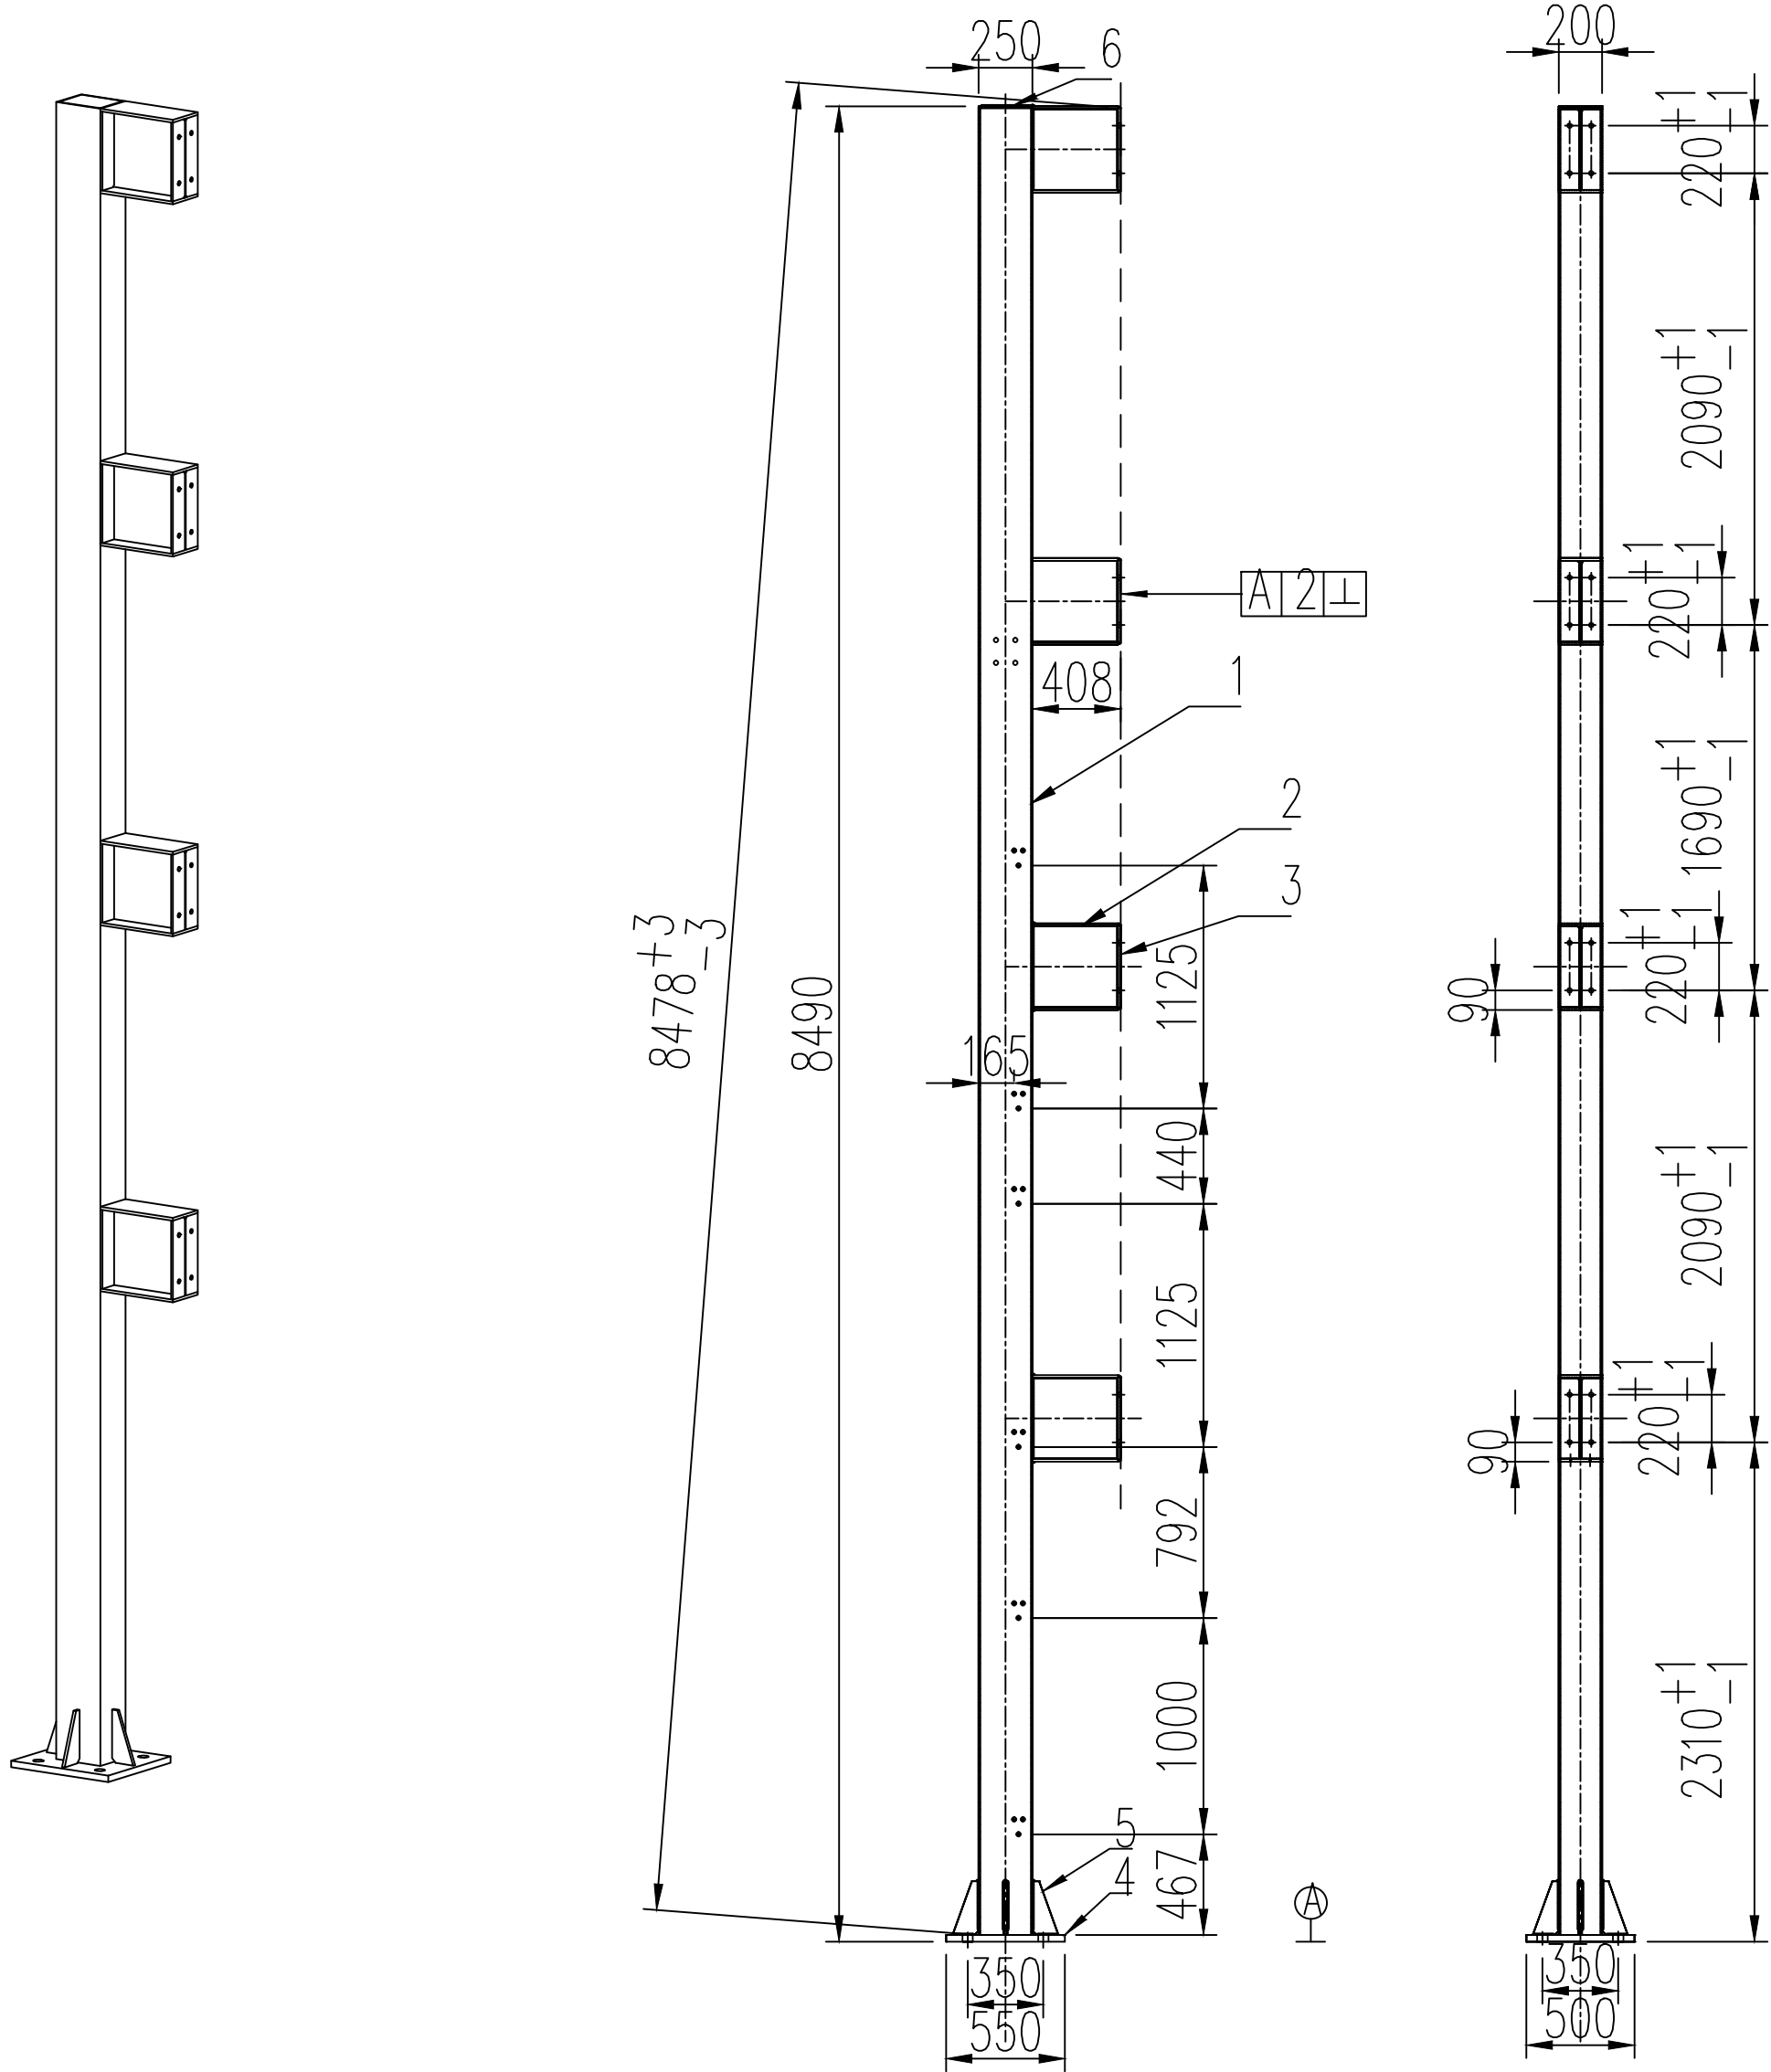

- 技术要求：
- 1.表面处理：喷漆前除锈要除干净，金属表面呈现金属光泽，不能留有油污锈迹；
 - 2.未注公差长度方向按±2mm,对角线方向±3mm；
 - 3.未注明焊高均为板厚的80%,皆为满焊；焊后校平
 - 4.焊接不允许有虚焊、漏焊、夹渣、裂纹等缺陷，焊接质量满足二级要求；
 - 5.焊缝修磨平整、圆滑、无飞边毛刺（特别是死角，转角交接处焊缝打磨光滑平整以便喷漆时能覆盖到）；

7					
6	PCX9-01-01-01-12	底部立柱封口板	1	Q235B	
5	PCX9-01-01-01-10	柱脚板加强肋	4	Q235B	
4	PCX9-01-01-01-9	底部立柱柱脚钢板	1	Q235B	
3	PCX9-01-01-01-8	底部立柱连接钢板	4	Q235B	
2	PCX9-01-01-01-3	底部立柱工字钢	4	Q235B	
1	PCX20-01-01-01-2	底部立柱钢通	1	Q235B	
序号	图号	名称	数量	备注	
标 记	处 数	修改日期	签 名	材料： 组焊件	
设 计		重量/Kg	446.55		
审 核		版 号	A		
批 准		比 例	1:60		
				深圳市奇见科技有限公司 SHENZHEN SIGHT TECHNOLOGY CO.,LTD	
				PCX型1层垂直循环类机械式停车设备	
				前左柱脚	
				PCX20-01-01-01	