
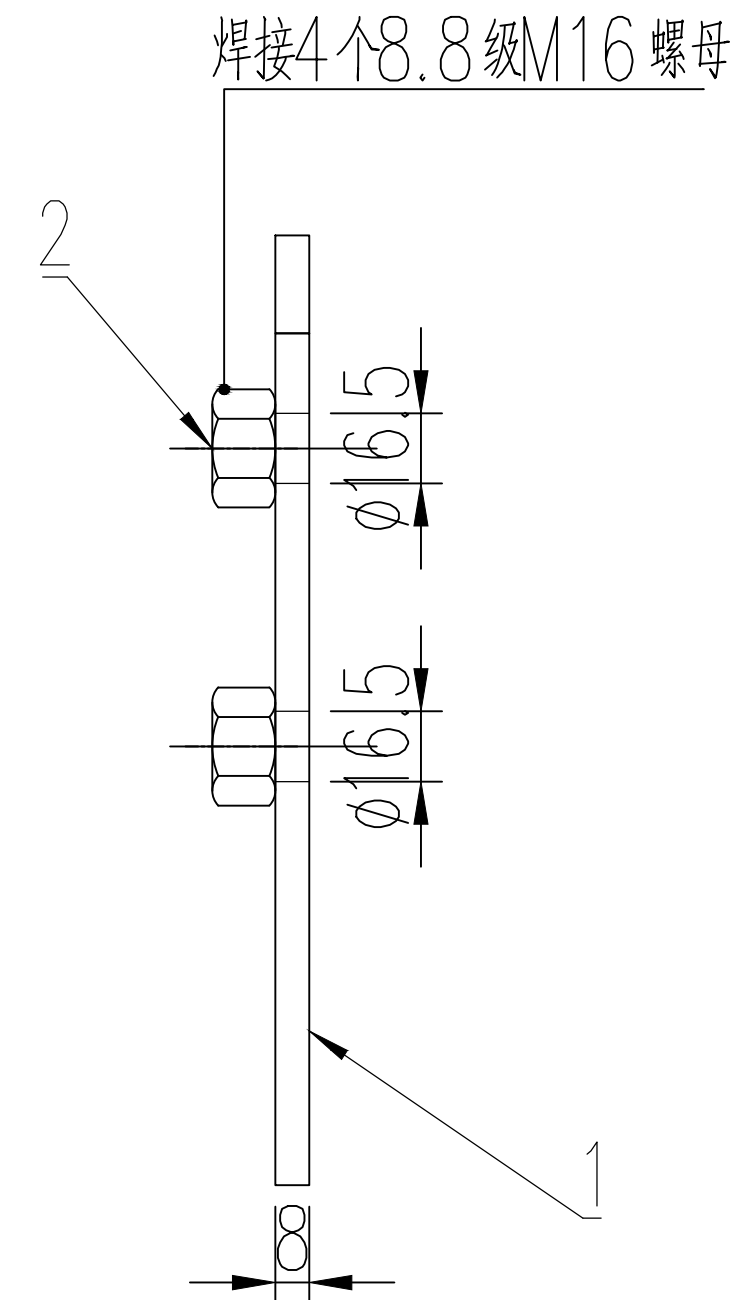


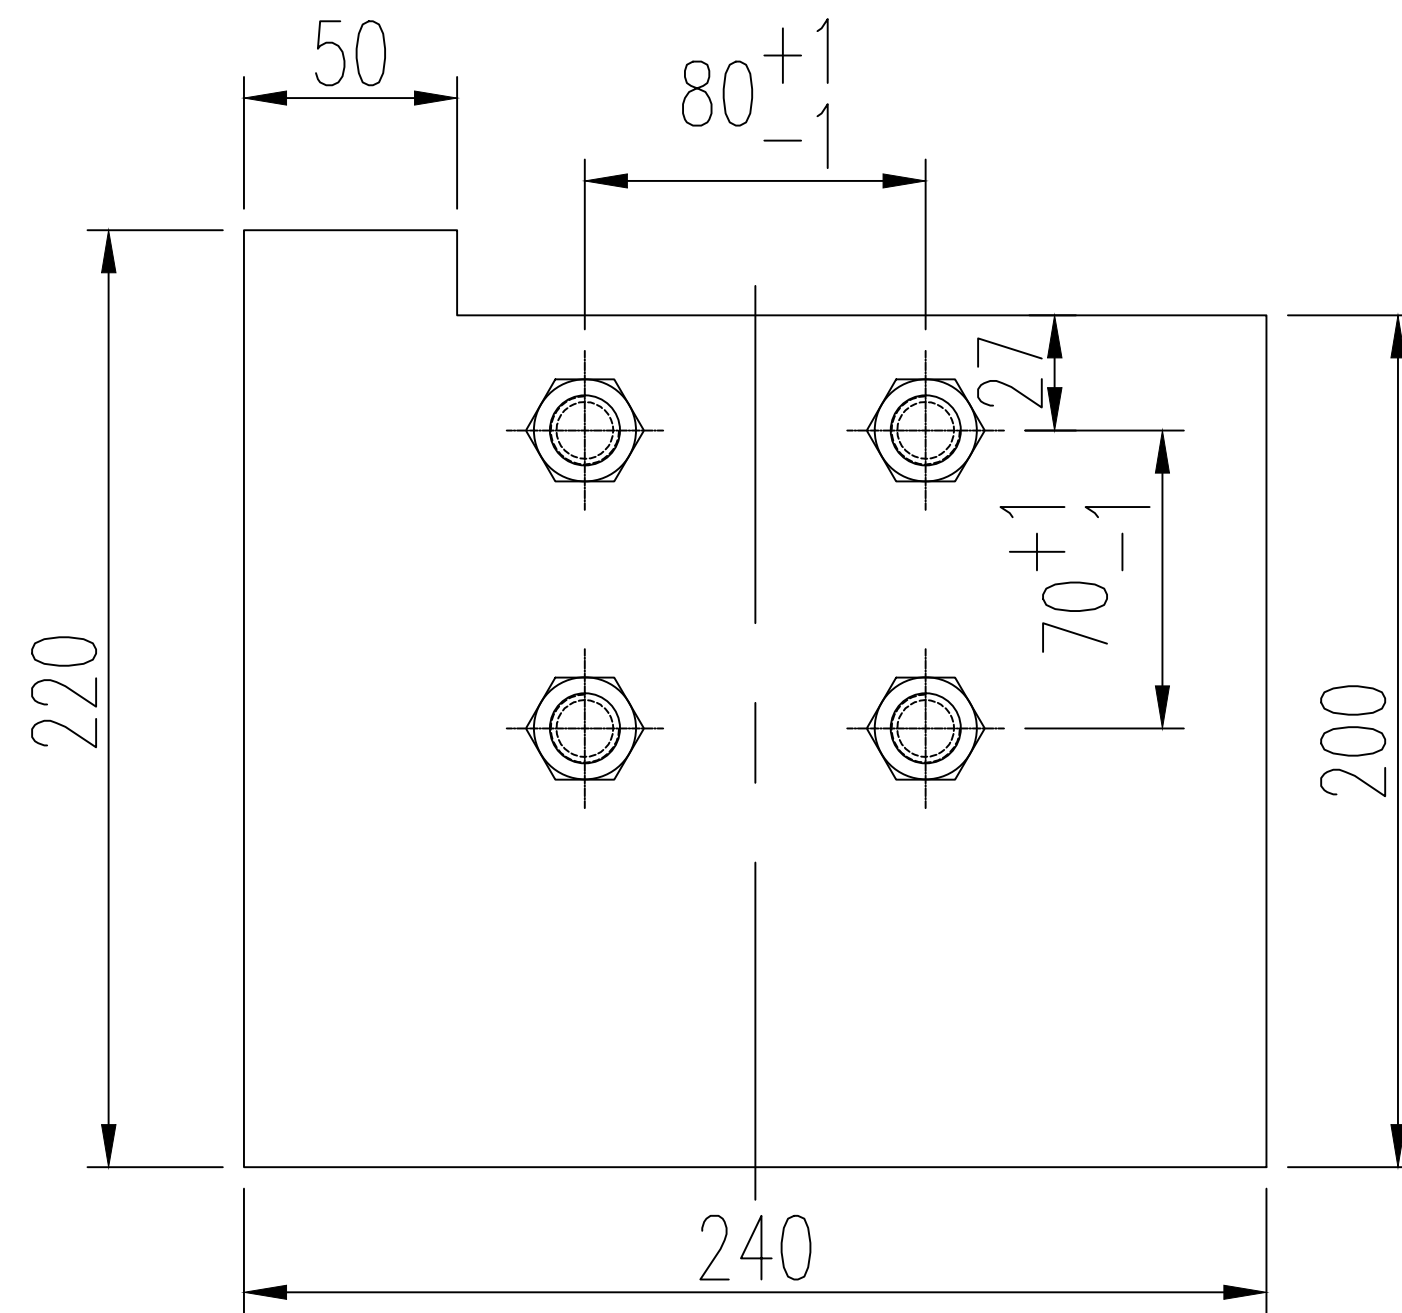

技术要求：
1. 下料长度精度为±0.5mm；
2. 未注明焊高均板厚的80%，皆为满焊；焊后校平

2		螺母M16		4	
1	PCX9-01-01-03-02-7-1	顶部封板1	Q235B/8*240*223	1	无图，本图代
序号	图号	名称	材料	数量	备注
		 深圳市奇见科技有限公司 SHENZHEN SIGHT TECHNOLOGY CO.,LTD 材料: 8mm厚钢板(Q235B)	PCX型9层垂直循环类机械式停车设备		
标 记	处 数		修 改 日 期	签 名	上片钢架立柱顶部封板1
设 计			重量/Kg	3.08	
审 核			版 号	A	
批 准			比 例	1:5	PCX9-01-01-03-02-7