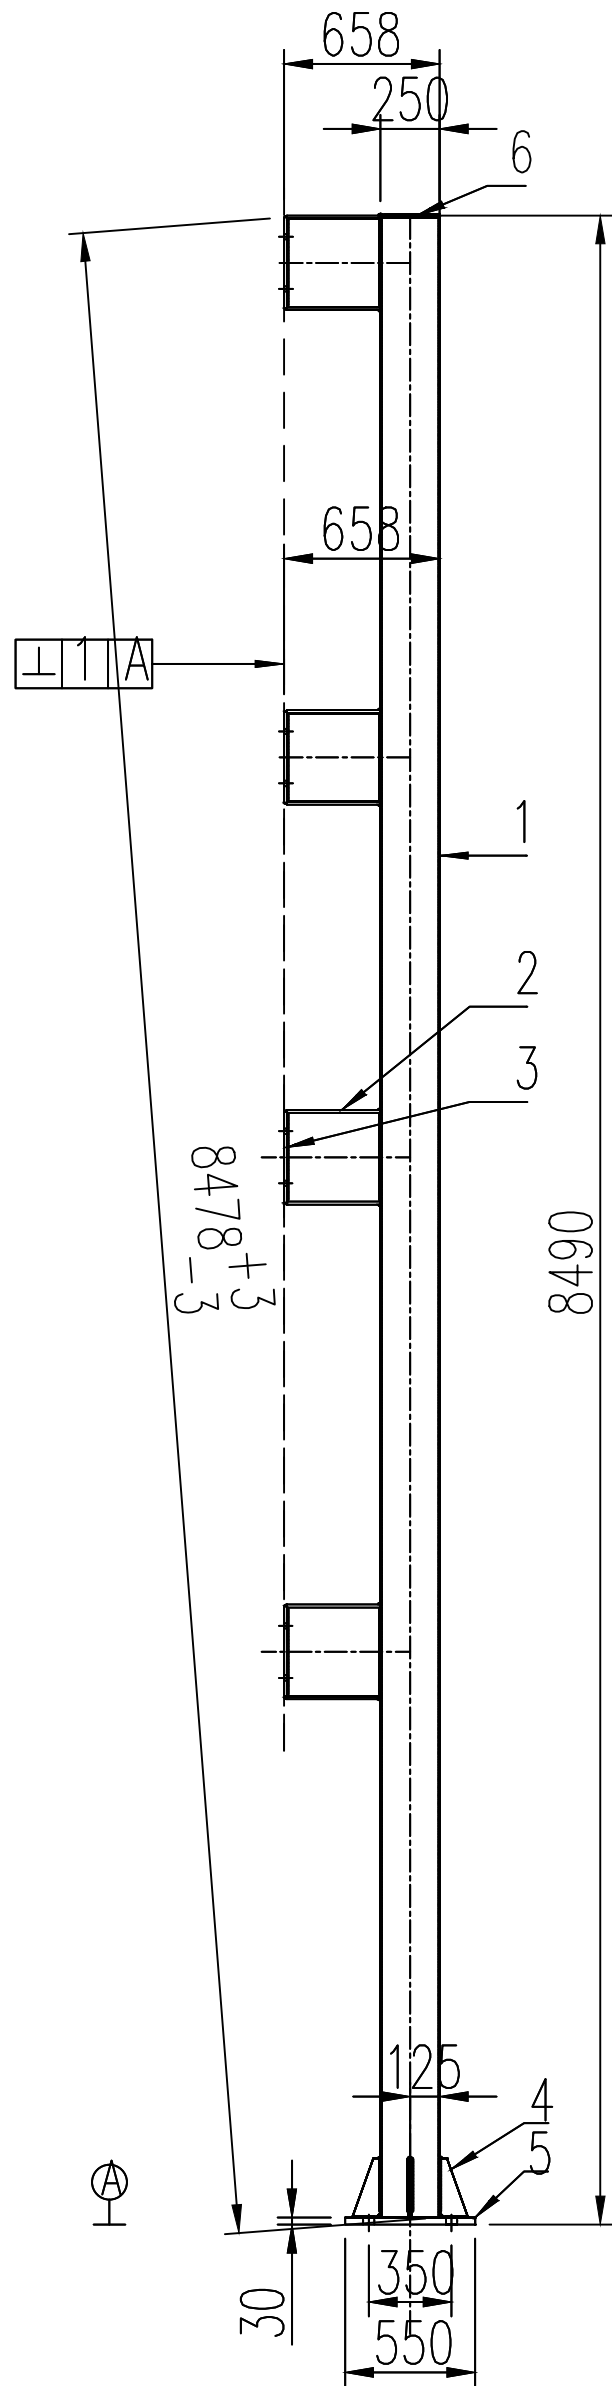
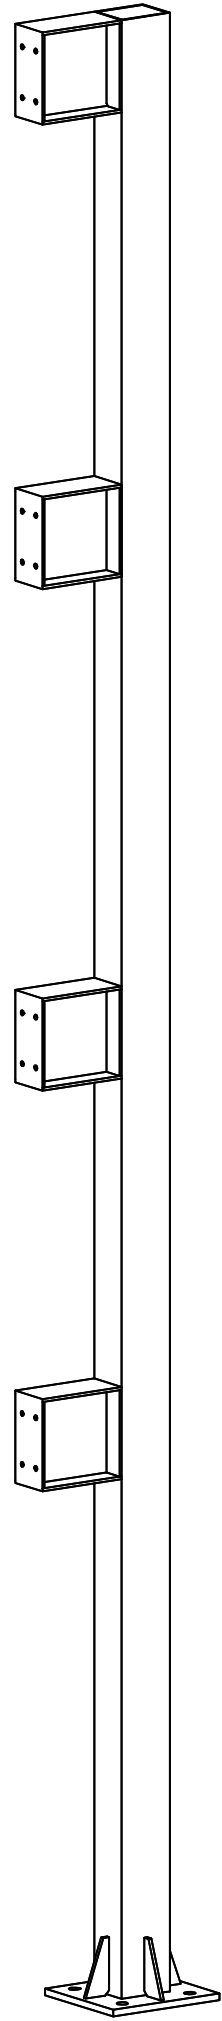


技术要求：

- 1. 表面处理：喷漆前除锈要除干净，金属表面呈现金属光泽，不能留有油污锈迹；
- 2. 未注公差长度方向按±2mm, 对角线方向±3mm；
- 3. 未注明焊高均为板厚的80%, 皆为满焊; 焊后校平
- 4. 焊接不允许有虚焊、漏焊、夹渣、裂纹等缺陷，焊接质量满足二级要求；
- 5. 焊缝修磨平整、圆滑、无飞边毛刺（特别是死角，转角交接处焊缝打磨光滑平整以便喷漆时能覆盖到）；

|    |                  |          |    |       |
|----|------------------|----------|----|-------|
| 6  | PCX9-01-01-01-12 | 底部立柱封口板  | 1  | Q235B |
| 5  | PCX9-01-01-01-9  | 底部立柱柱脚钢板 | 1  | Q235B |
| 4  | PCX9-01-01-01-10 | 柱脚板加强肋   | 4  | Q235B |
| 3  | PCX9-01-01-01-8  | 底部立柱连接钢板 | 3  | Q235B |
| 2  | PCX9-01-01-01-3  | 底部立柱工字钢  | 3  | Q235B |
| 1  | PCX20-01-02-01-3 | 后片底部立柱钢通 | 1  | Q235B |
| 序号 | 图号               | 名称       | 数量 | 备注    |

|     |     |       |        |   |                    |
|-----|-----|-------|--------|---|--------------------|
|     |     |       |        |  深圳市奇见科技有限公司<br>SHENZHEN SIGHT TECHNOLOGY CO.,LTD | PCX型1层垂直循环类机械式停车设备 |
| 标 记 | 处 数 | 修改日期  | 签 名    |   |                    |
| 设 计 |     | 重量/Kg | 446.55 | 材料：<br>组焊件   | 底部立柱               |
| 审 核 |     | 版 号   | A      |   | PCX20-01-02-01     |
| 批 准 |     | 比 例   | 1:60   |   |                    |