
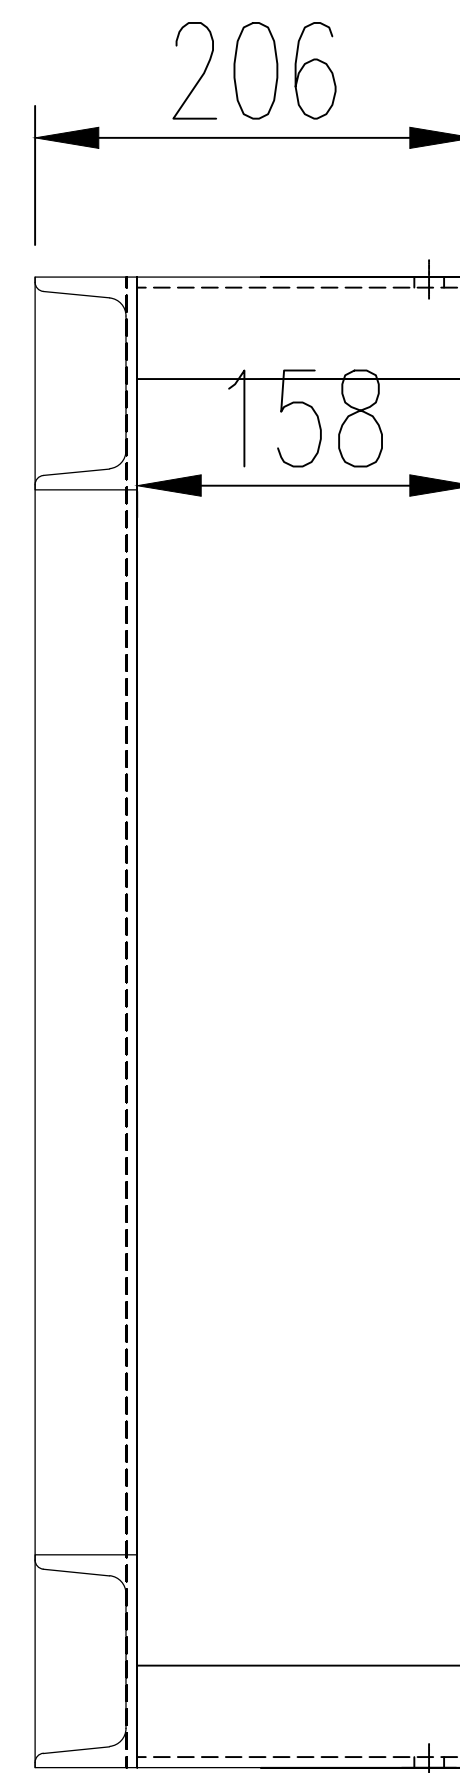


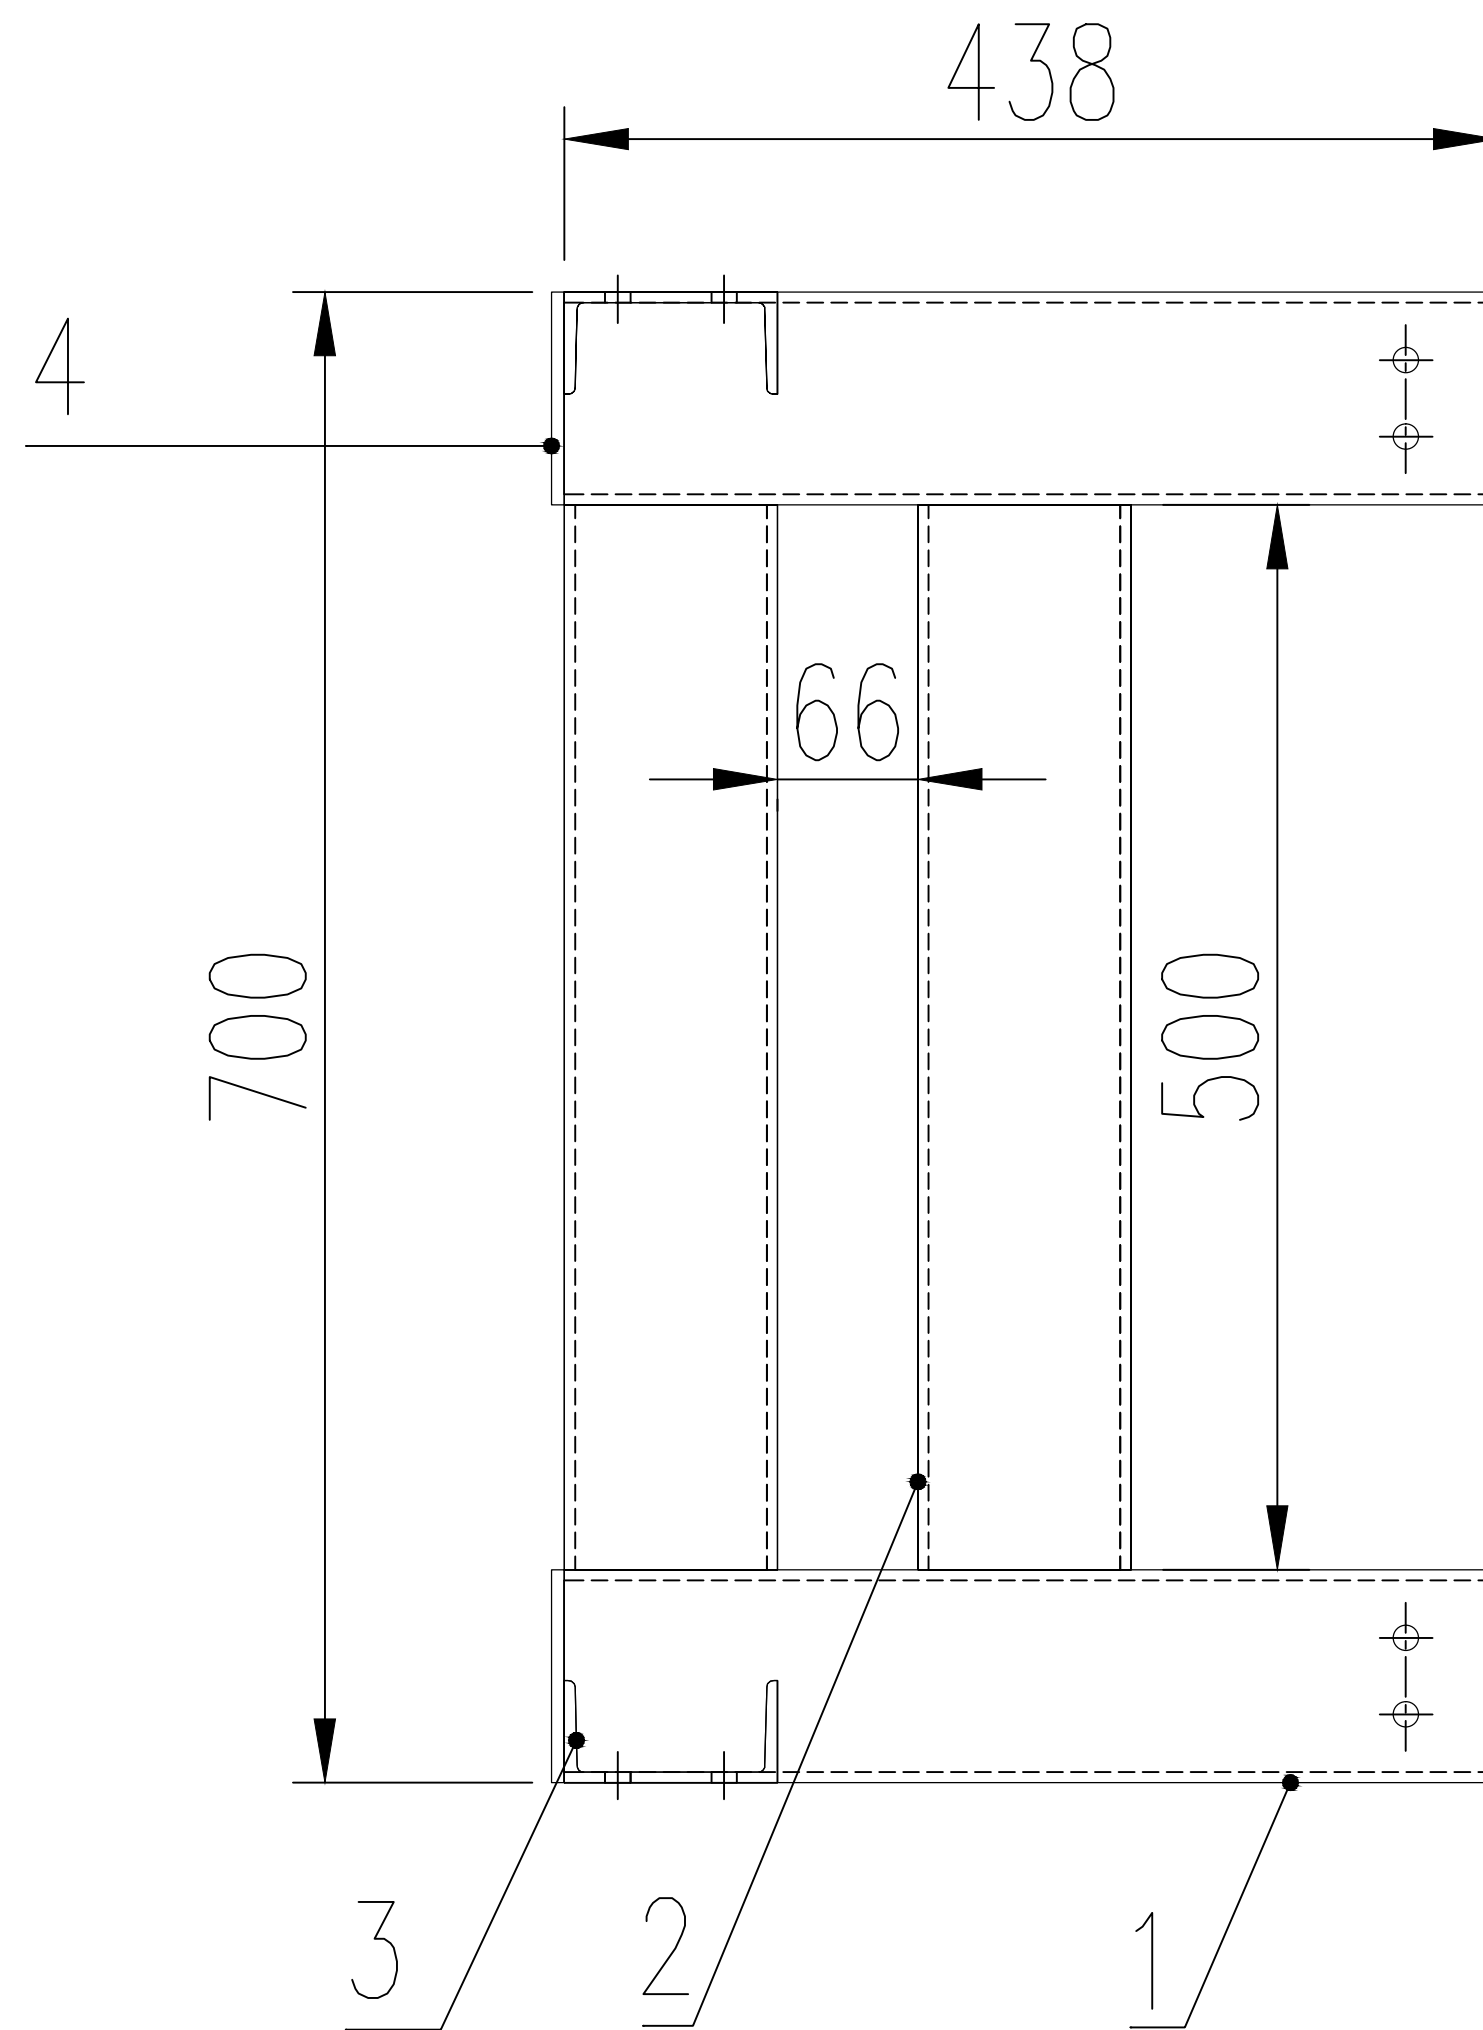

技术要求：

1. 表面处理：喷漆前除锈要除干净，金属表面呈现金属光泽，不能留有油污锈迹；
2. 表面喷漆处理
3. 未注公差长度方向按 $\pm 2\text{mm}$ ，对角线方向 $\pm 3\text{mm}$ ；
4. 未注明焊高均为 $6\text{mm}$ ，皆为满焊；
5. 焊接不允许有虚焊、漏焊、夹渣、裂纹等缺陷，焊接质量满足二级要求；
6. 焊缝修磨平整、圆滑、无飞边毛刺（特别是死角，转角交接处焊缝打磨光滑平整以便喷漆时能覆盖到）；

|        |                 |           |      |                                               |
|--------|-----------------|-----------|------|-----------------------------------------------|
| 4      | PCX9-01-02-04-4 | 封口板03     | 2    |                                               |
| 3      | PCX9-01-02-04-3 | 防摆侧向支架钢通3 | 2    |                                               |
| 2      | PCX9-01-02-04-2 | 防摆侧向支架钢通2 | 2    |                                               |
| 1      | PCX9-01-02-05-1 | 防摆侧向支架钢通4 | 2    |                                               |
| 序号     | 图号              | 名称        | 数量   | 备注                                            |
|        |                 |           |      |                                               |
| 标 记    | 处 数             | 修改日期      | 签 名  | PCX9型7层垂直循环类机械式停车设备<br>防摆支架2<br>PCX9-01-02-05 |
| 设 计    |                 | 重量/Kg     | 23.4 |                                               |
| 审 核    |                 | 版 号       | A    |                                               |
| 批 准    |                 | 比 例       | 1:10 |                                               |
| 材料：组焊件 |                 |           |      |                                               |