


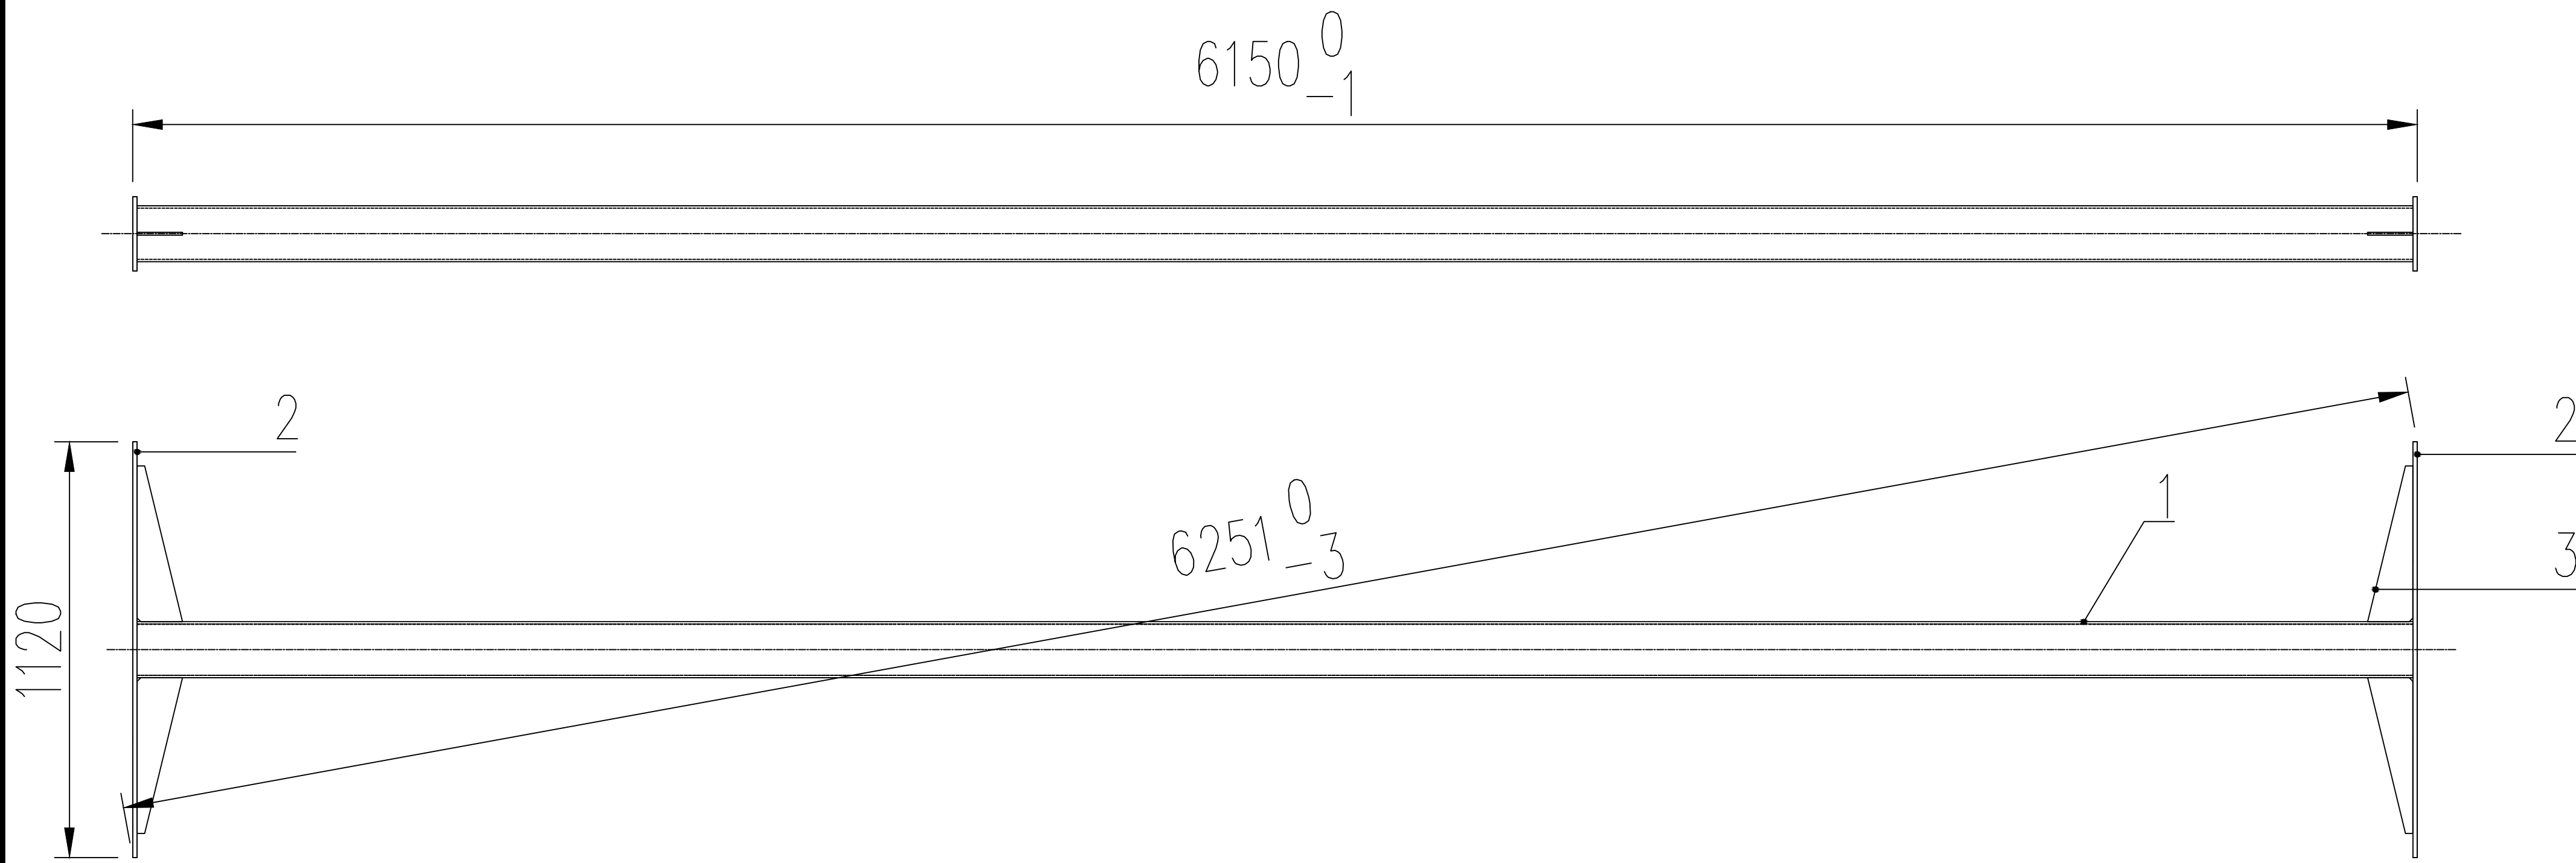

- 技术要求：
- 1. 表面处理：喷漆前除锈要除干净，金属表面呈现金属光泽，不能留有油污锈迹；
 - 2. 未注公差长度方向±1mm, 对角线方向±2mm；
 - 3. 未注明焊高均为6mm, 皆为满焊；
 - 4. 焊接不允许有虚焊、漏焊、夹渣、裂纹等缺陷，焊接质量满足二级要求；
 - 5. 焊缝修磨平整、圆滑、无飞边毛刺（特别是死角，转角交接处焊缝打磨光滑平整以便喷漆时能覆盖到）；

3	PCX9-01-02-14	中横梁加强筋	4	
2	PCX9-01-02-14	中横梁钢板	2	
1	PCX9-01-02-14	中横梁钢通1	1	
序号	图号	名称	数量	备注
标 记	处 数	修改日期	签 名	PCX9型7层垂直循环类机械式停车设备 中横梁1 PCX9-01-02-14
设 计		重量/Kg	211.47	
审 核		版 号	A	
批 准		比 例	1:35	
材料：组焊件				