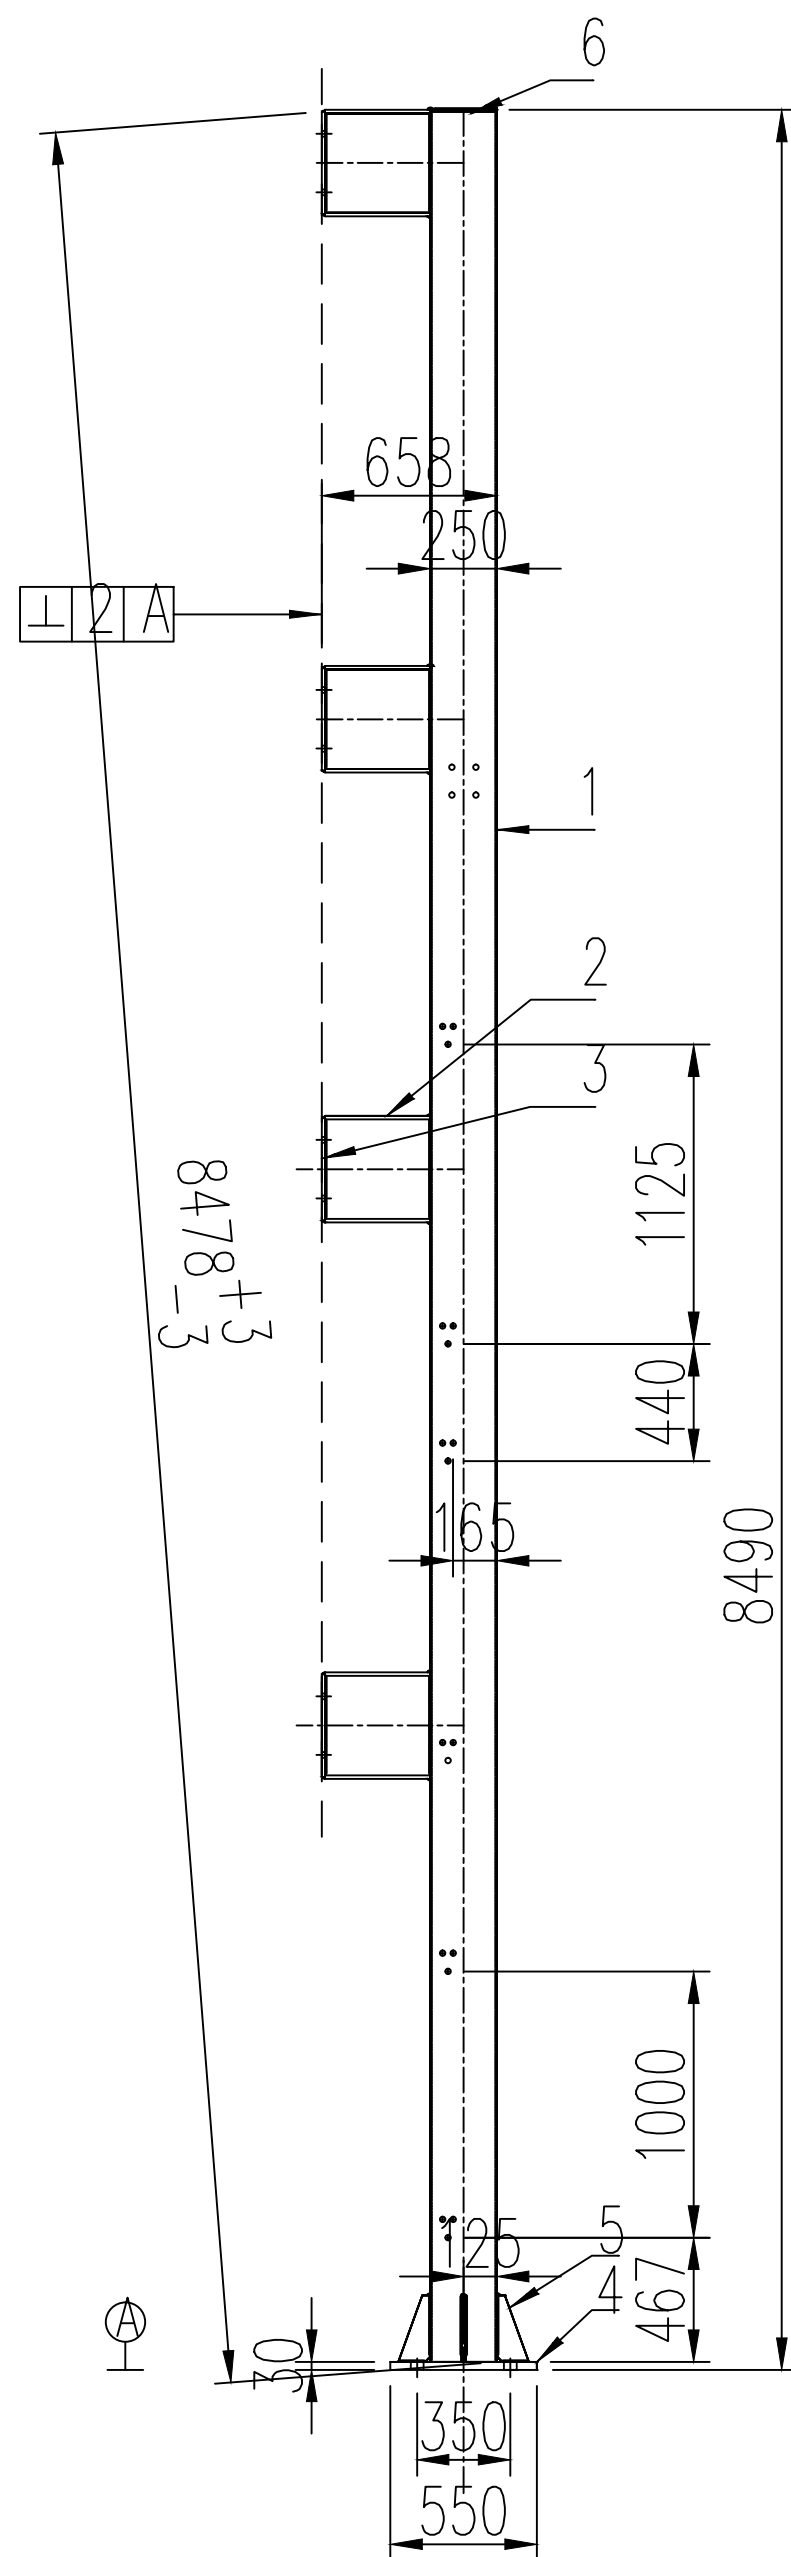
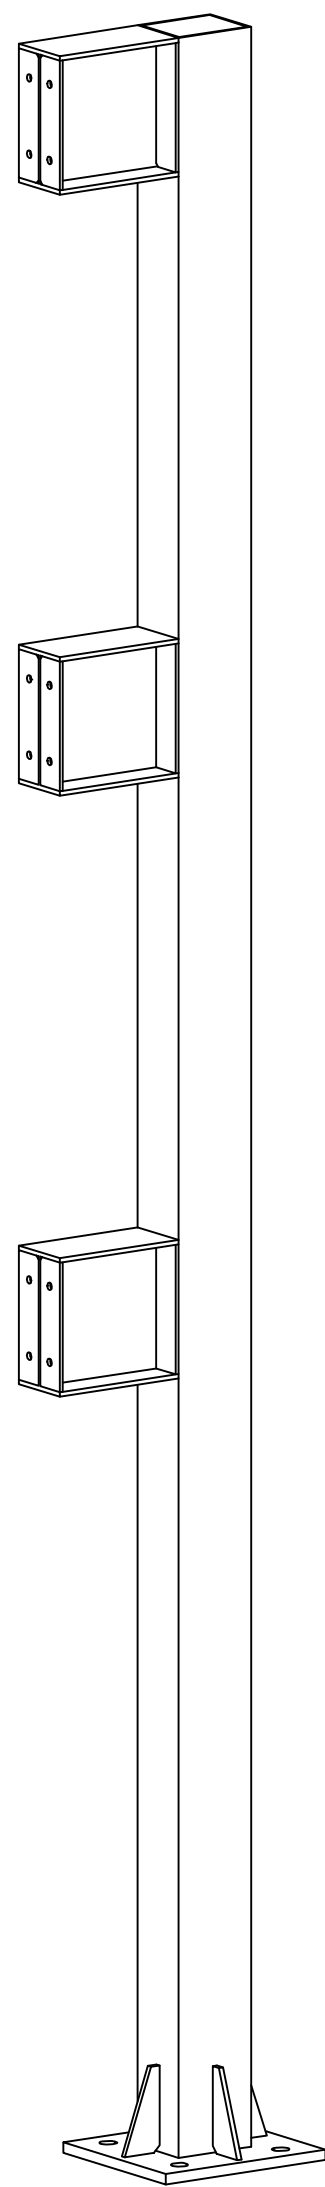


技术要求:

1. 表面处理: 喷漆前除锈要除干净, 金属表面呈现金属光泽, 不能留有油污锈迹;
2. 未注公差长度方向按 $\pm 2\text{mm}$, 对角线方向 $\pm 3\text{mm}$;
3. 未注明焊高均为板厚的80%, 皆为满焊; 焊后校平
4. 焊接不允许有虚焊、漏焊、夹渣、裂纹等缺陷, 焊接质量满足二级要求;
5. 焊缝修磨平整、圆滑、无飞边毛刺(特别是死角, 转角交接处焊缝打磨光滑平整以便喷漆时能覆盖到);

6	PCX9-01-01-01-12	底部立柱封口板	1	Q235B
5	PCX9-01-01-01-10	柱脚板加强肋	4	Q235B
4	PCX9-01-01-01-9	底部立柱柱脚钢板	1	Q235B
3	PCX9-01-01-01-8	底部立柱连接钢板	3	Q235B
2	PCX9-01-01-01-3	底部立柱工字钢	3	Q235B
1	PCX20-01-01-02-1	底部立柱钢通	1	Q235B
序号	图号	名称	数量	备注

				 深圳市奇见科技有限公司 SHENZHEN SIGHT TECHNOLOGY CO.,LTD	PCX型1层垂直循环类机械式停车设备
标 记	处 数	修改日期	签 名		
设 计		重量/Kg	446.55	材料: 组焊件	前右柱脚
审 核		版 号	A		PCX20-01-01-02
批 准		比 例	1:60		