


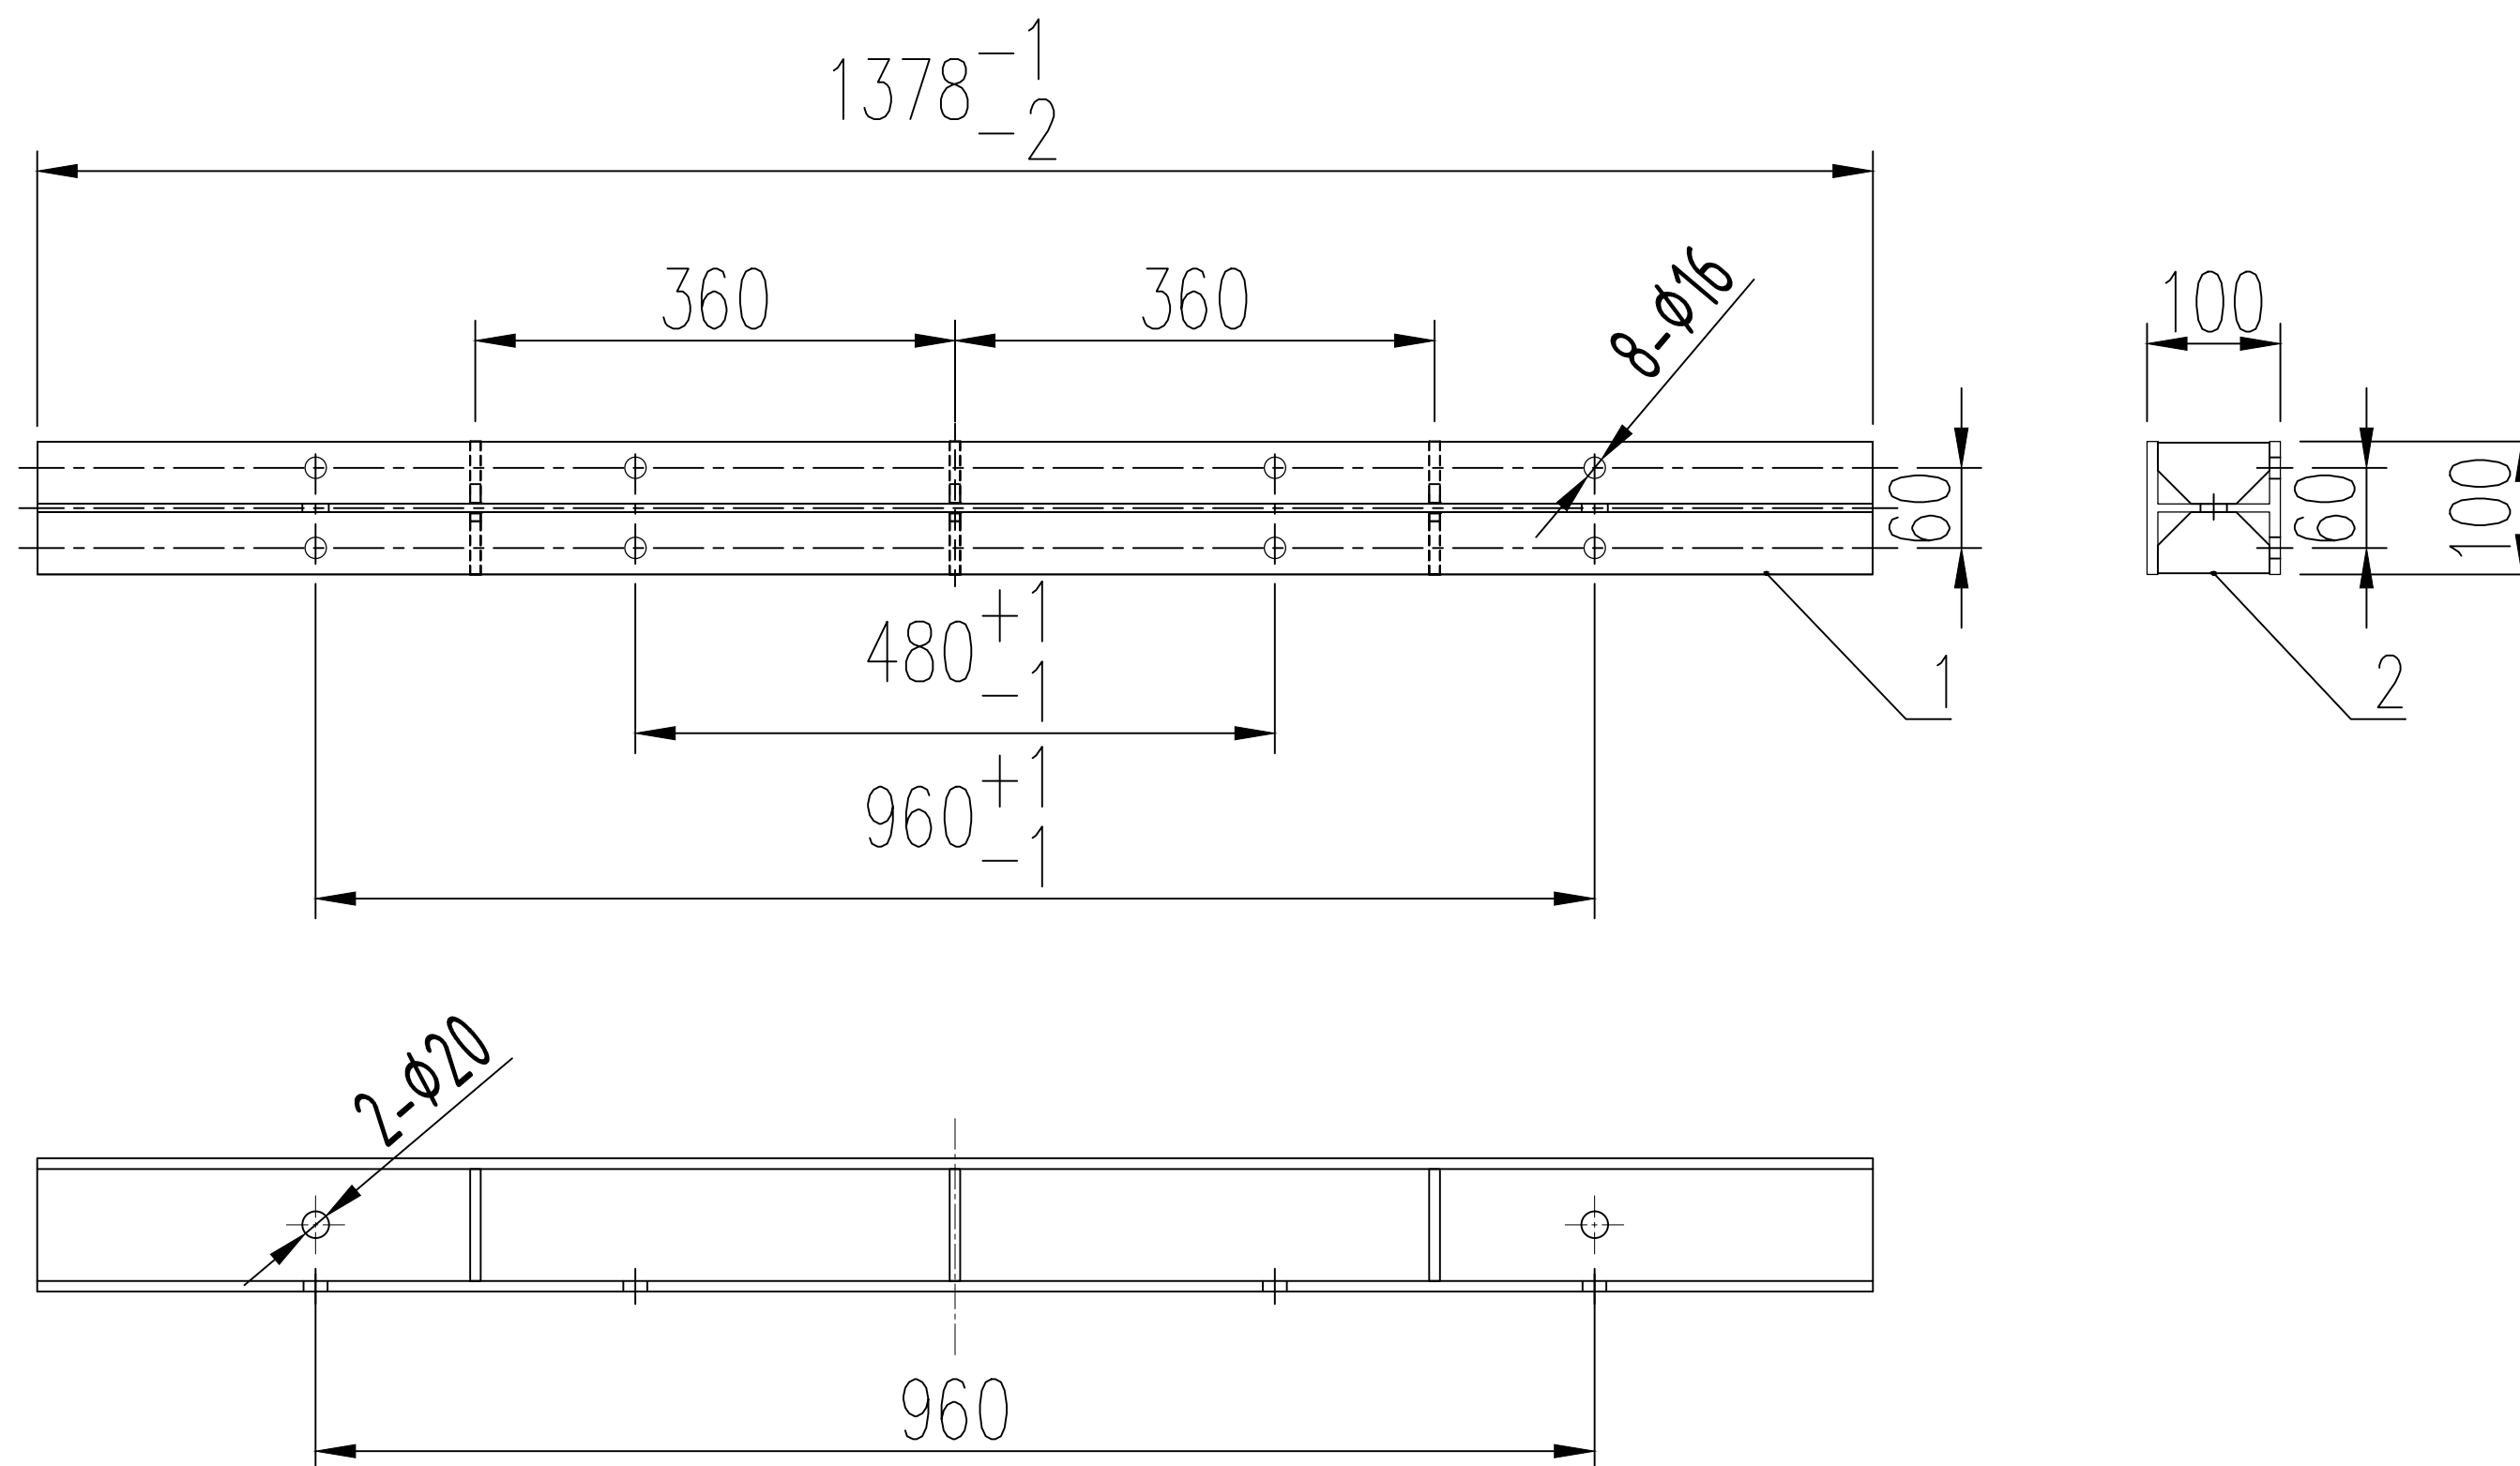

技术要求：

2	PCX9-01-01-03-01-16-2	8mm 厚钢板	Q235B	6	
1	PCX9-01-01-03-01-16-1	100*100*6*8mm H型钢	Q235B	1	
序号	图号	名称	材料	数量	备注
标 记	处 数	修改日期	签 名	PCX 型9层垂直循环类机械式停车设备	
设 计		重量/Kg	23.7		
审 核		版 号	A		
批 准		比 例	1:15		
深圳市奇见科技有限公司 SHENZHEN SIGHT TECHNOLOGY CO.,LTD				H 型钢横梁1	
材料：组焊件				PCX9-01-01-03-01-16	