


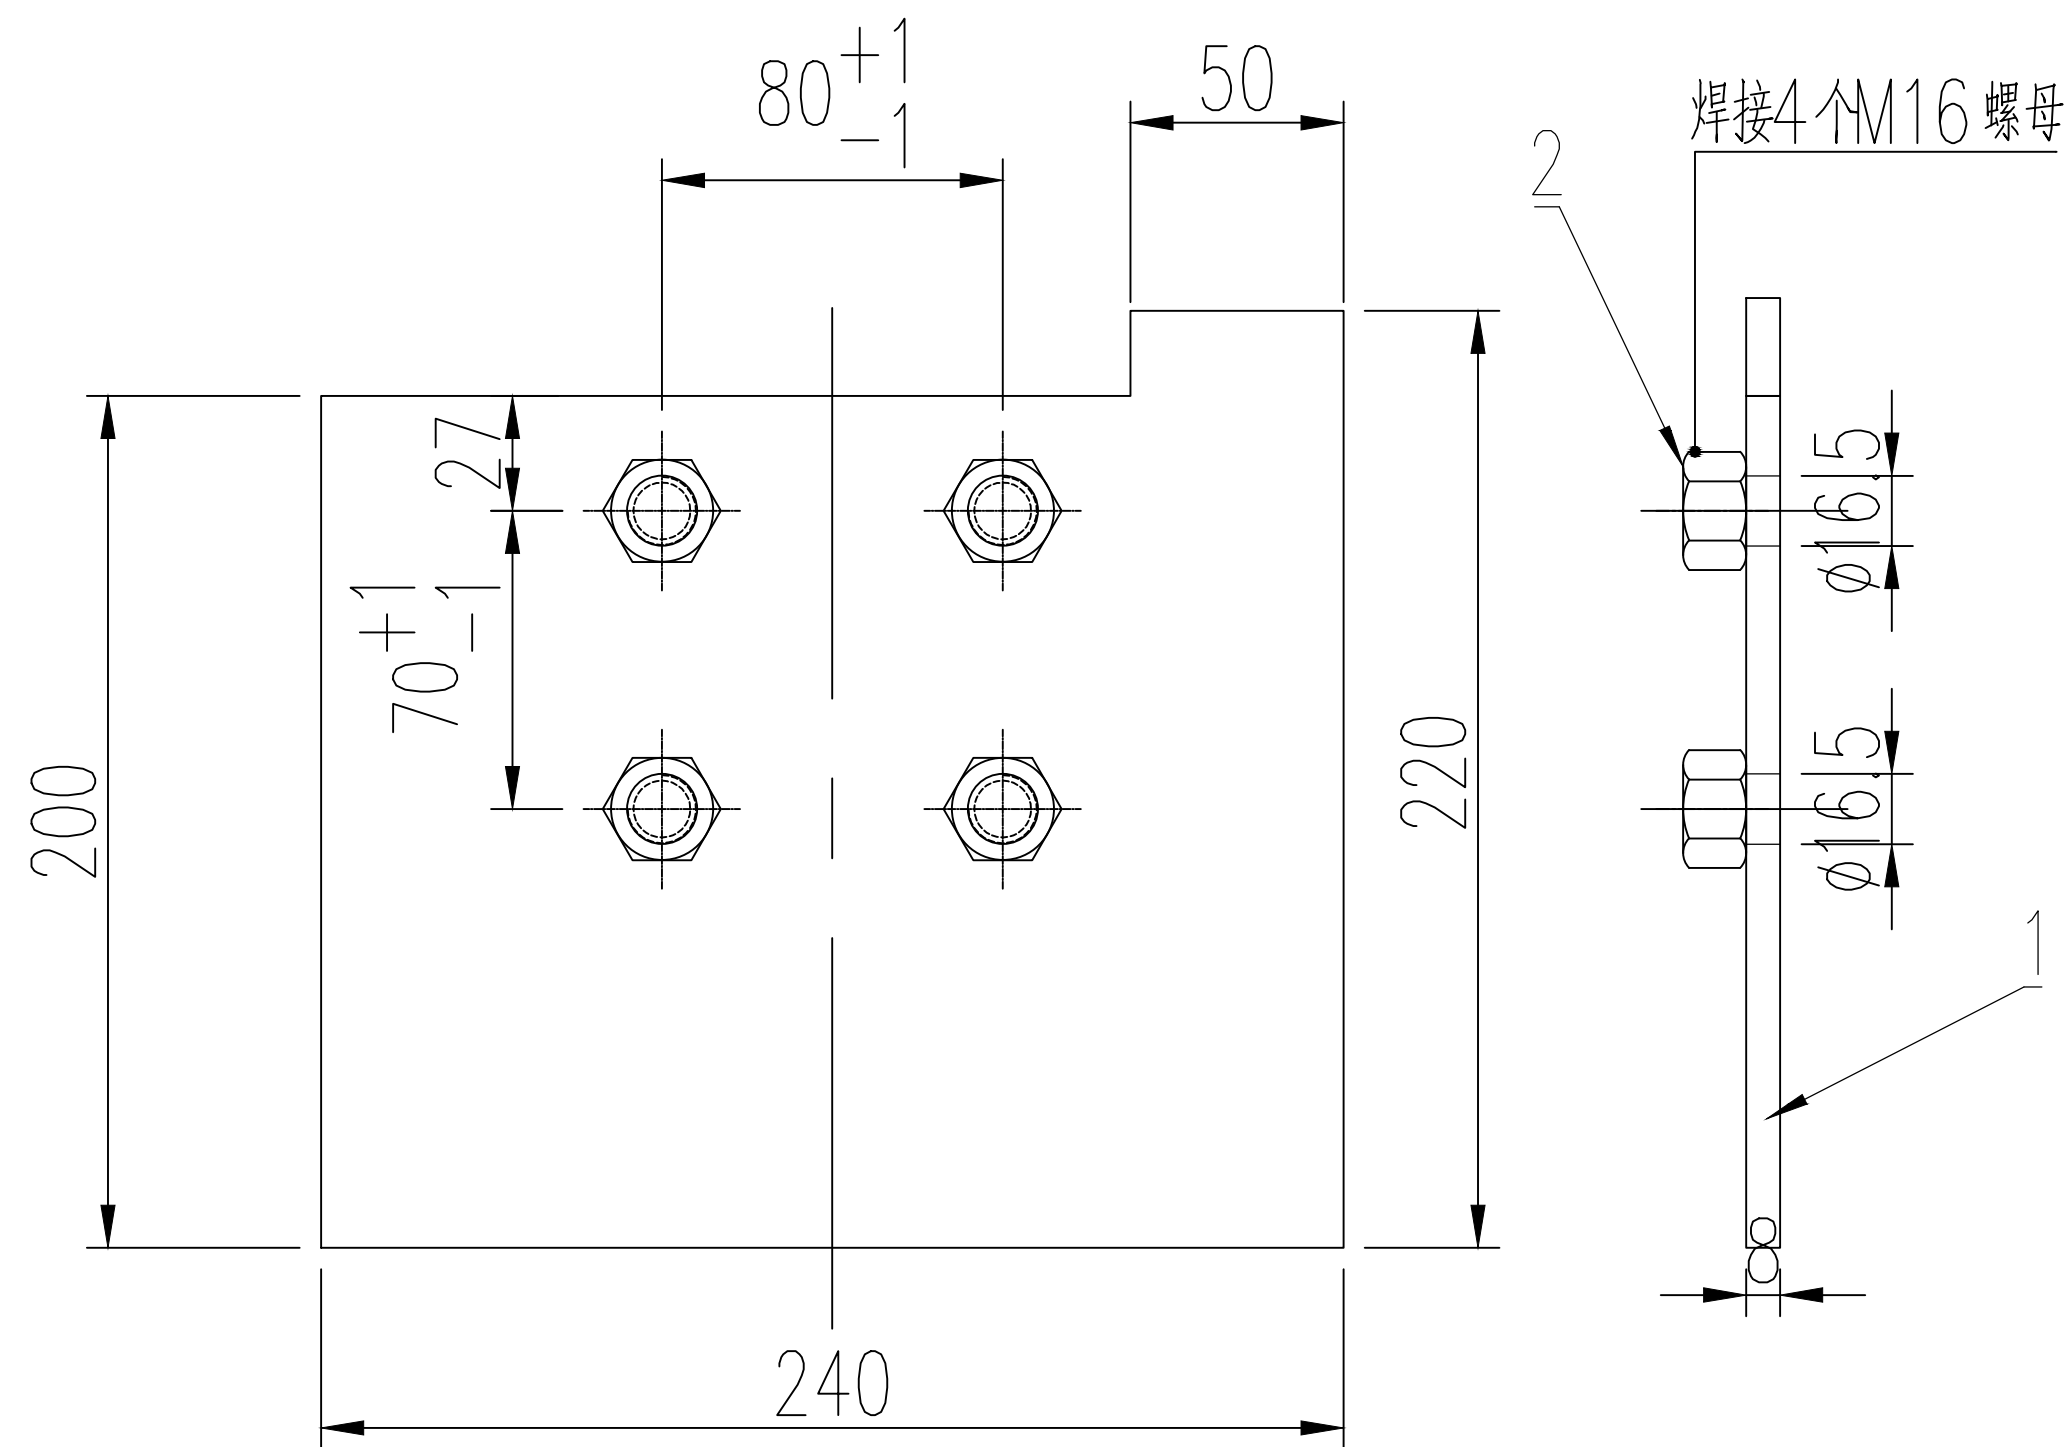

技术要求：
1. 下料长度精度为±0.5mm；
2. 未注明焊高均板厚的80%，皆为满焊；焊后校平

2		螺母M16		4	
1	PCX9-01-01-03-02-8-1	顶部封板1	Q235B/8*240*223	1	无图，本图代
序号	图号	名称	材料	数量	备注
标 记	处 数	修改日期	签 名	PCX型9层垂直循环类机械式停车设备 上片钢架立柱顶部封板2 PCX9-01-01-03-02-8	
设 计		重量/Kg	3.08		
审 核		版 号	A		
批 准		比 例	1:5		
深圳市奇见科技有限公司 SHENZHEN SIGHT TECHNOLOGY CO.,LTD 材料：8mm厚钢板（Q235B）					