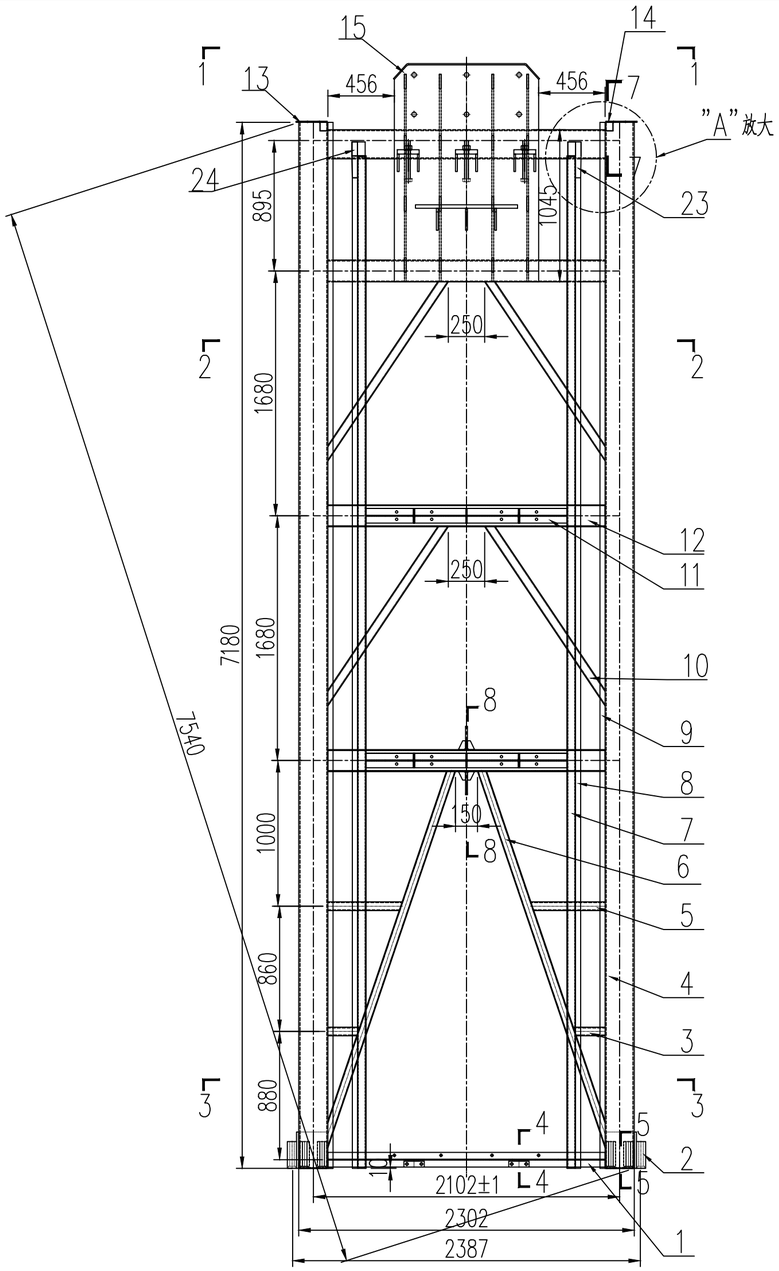

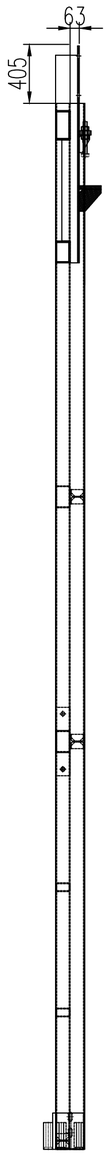

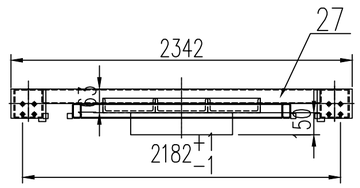

1—1

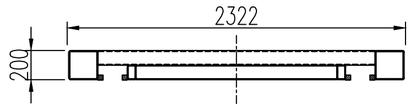

2—2

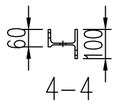

4—4

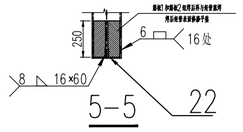

5—5

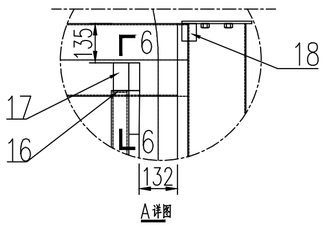

A详图

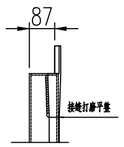

6—6

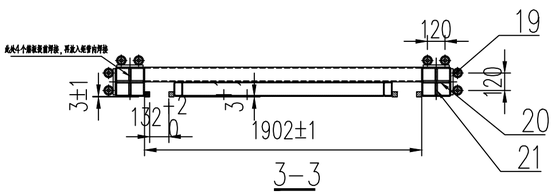

3—3

7—7

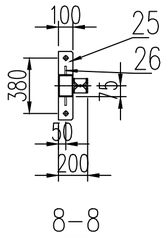

8—8

技术要求：

1. 表面处理：喷漆前除锈要除干净，金属表面呈现金属光泽，不能留有油污锈迹；
2. 未注公差长度方向按±2mm，对角线方向±3mm；
4. 未注明焊高均板厚的80%，皆为满焊，焊后校平
5. 焊接不允许有虚焊、漏焊、夹渣、裂纹等缺陷，焊接质量满足二级要求；
6. 焊缝修磨平整、圆滑、无飞边毛刺（特别是死角，转角交接处焊缝打磨光滑平整以便喷漆时能覆盖到）；
7. 喷漆时注意保护螺纹孔。

序号	图号	名称	数量	备注
27	PCX9-01-01-03-01-32	下片钢架横梁2	1	
26	PCX9-01-01-03-01-46	斜拉杆连接板筋板	4	
25	PCX9-01-01-03-01-45	斜拉连接钢板2	2	
24	PCX-01-01-03-01-40	左侧上部导轨连接钢块	1	
23	PCX-01-01-03-01-39	右侧上部导轨连接钢块	1	
22	PCX9-01-01-03-01-29	封口板3	2	
21	PCX9-01-01-03-01-25	连接处筋板2	4	
20	PCX9-01-01-03-01-24	连接处筋板1	2	
19	PCX9-01-01-03-01-23	连接套筒衬板	4	
18	PCX9-01-01-03-02-11	导向钢板	2	
17	PCX9-01-01-03-02-10	支撑钢块	2	
16	PCX9-01-01-03-01-44	封口板2	4	
15	PCX9-01-01-03-02-9	上部导轨支撑钢架	1	
14	PCX9-01-01-03-02-8	上片钢架立柱顶部封板2	1	
13	PCX9-01-01-03-02-7	上片钢架立柱顶部封板1	1	
12	PCX9-01-01-03-01-17	框架中部横梁	3	
11	PCX9-01-01-03-01-16	H型钢横梁1	2	
10	PCX9-01-01-03-02-6	上框架斜撑	4	
9	PCX9-01-01-03-02-5	竖向外导轨	2	
8	PCX9-01-01-03-02-4	竖向内导轨	2	
7	PCX9-01-01-03-02-3	竖向导轨依附钢通	2	
6	PCX9-01-01-03-01-12	框架斜撑	2	
5	PCX9-01-01-03-01-14	中部框架斜撑4	2	
4	PCX20-01-01-03-02-2	框架立柱1	2	
3	PCX9-01-01-03-01-13	中部框架斜撑3	2	
2	PCX9-01-01-03-02-1	钢架连接套筒1	8	
1	PCX9-01-01-03-01-28	钢架拼接处H型钢	1	

标记	处数	修改日期	签名	深圳市奇见科技有限公司 SHENZHEN SIGHT TECHNOLOGY CO.,LTD	PCX型1层垂直循环类机械式停车设备
设计		重量/Kg	3181.2	材料：焊接件	前片主框架2
审核		版号	A		PCX20-01-01-03-02
批准		比例	1:1		